


План елементів покрівлі навісу М 1:200

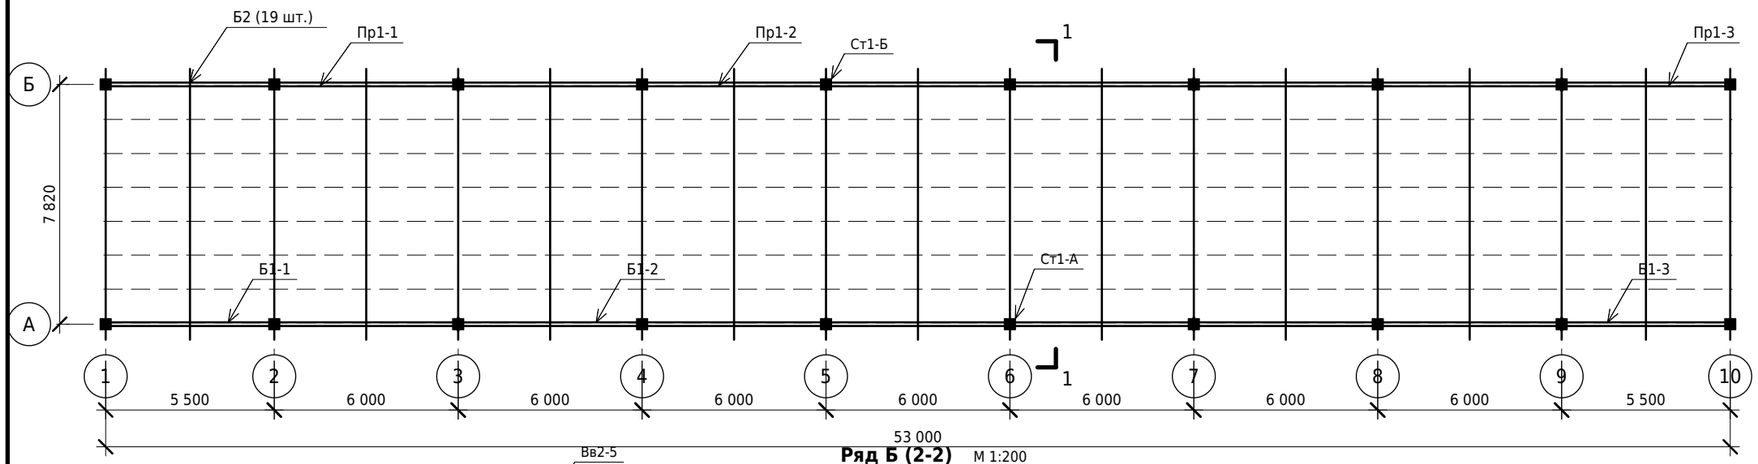

Ряд Б (2-2) М 1:200

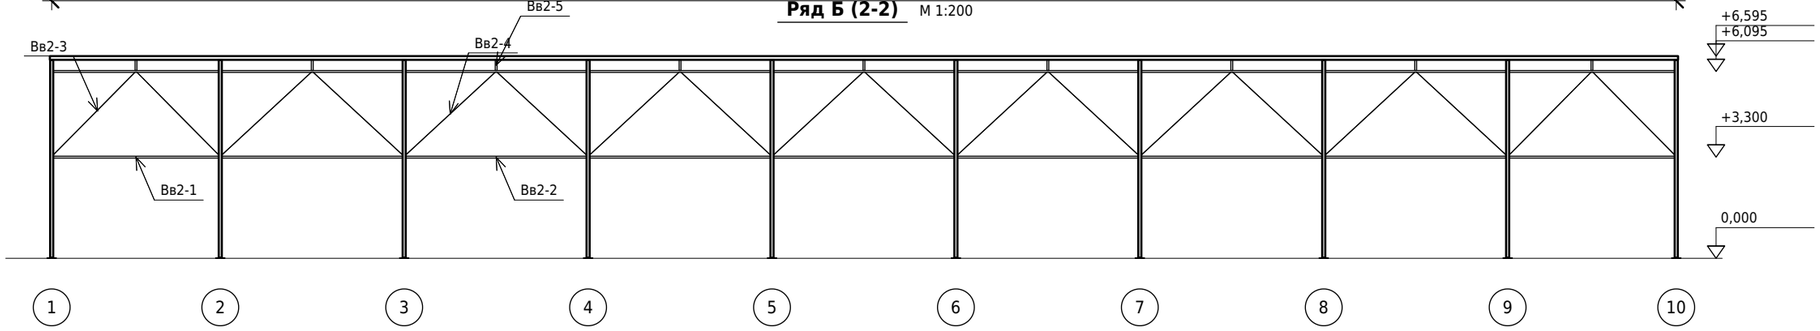

Ряд А (5-5) М 1:200

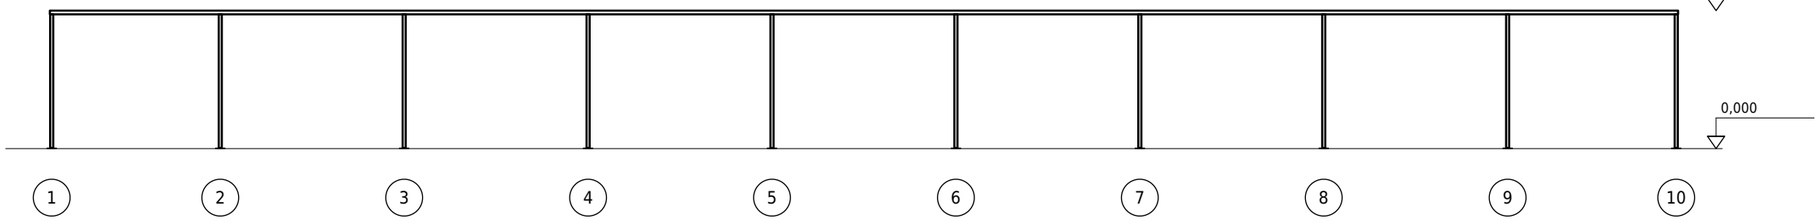


Вузли 1, 2 — арк. 6; вузол 3 — арк. 5;
вузли 4, 5 (ферма ряду Б) — арк. 7.

Вершина підкосів Вв1 — посередині прольоту,
зазор між підкосами під кроквою — 10 мм.

Б1 — поздовжні балки по рядах А і Б,
Б2 — крокви з кроком 3,0 м (2,75 м біля торців).

Розріз 1-1 М 1:100

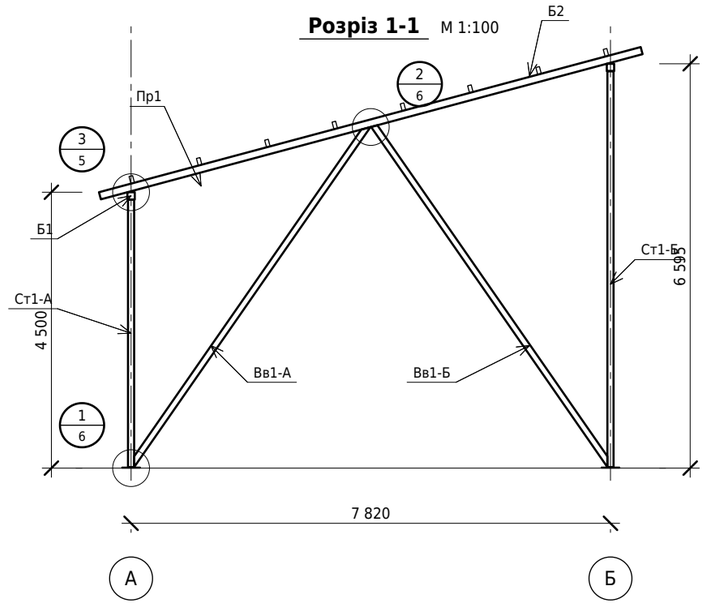

Зм.	Кільк.	Арк.	№ док.	Підпис	Дата
Розробив					
Перевірив					
Н. контр.					
ГІП					

36/26-КМД

Улаштування джерела резервного живлення модульної сонячної електростанції (СЕС), сел. Гостомель, вул. Свято-Покровська, 81Б

Стадія	Аркуш	Аркушів
Р	2	12

Схема розташування елементів

Формат А3