

Ст1-А (10 шт.)

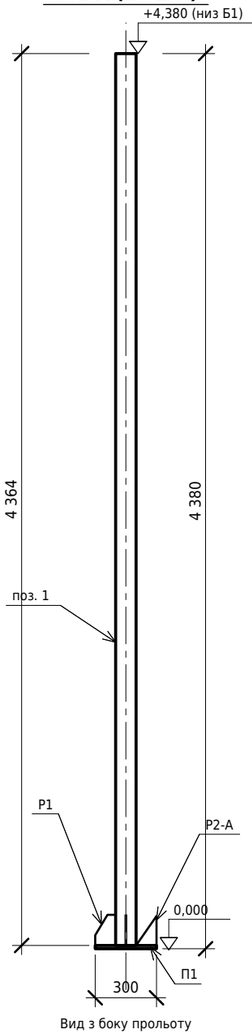


Вид з боку прольоту

Ст1-Б (10 шт.)

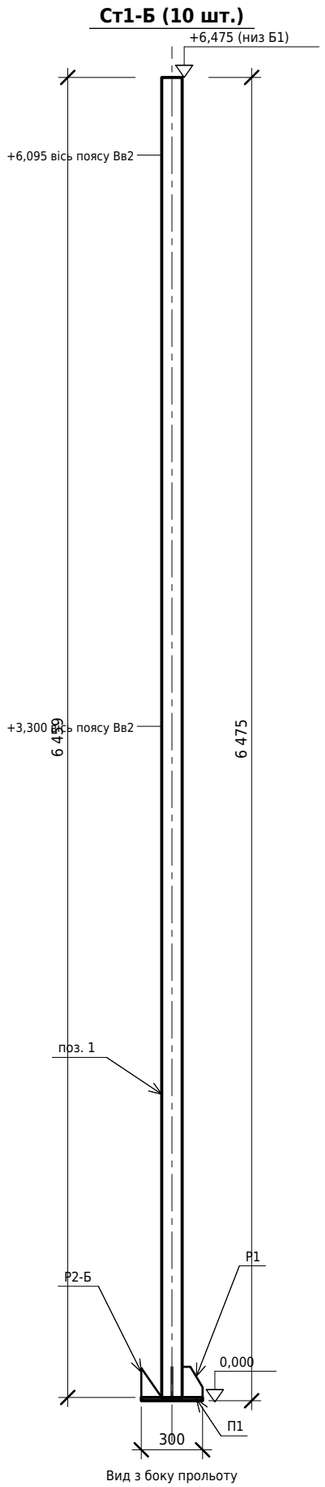


Вид з боку прольоту

База стійки (ряд А; ряд Б — дзеркально) М 1:5

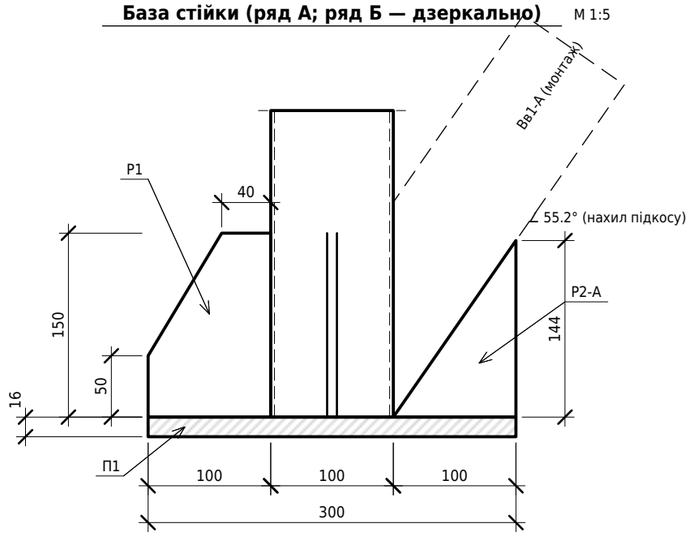

Шви: Ст1 до П1 — по контуру, kf = 4; ребра до П1 і Ст1 — з двох боків, kf = 4.

План бази М 1:5

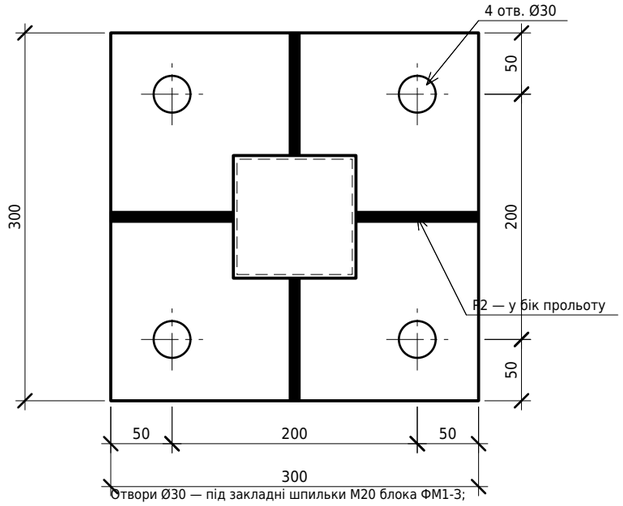

Отвори Ø30 — під закладні шпильки М20 блока ФМ1-3;

після вивіряння — шайби Ш1 приварити до П1 (арк. 8).

Склад марок

Марка	Поз.	Найменування	К-сть	Маса 1 шт., кг	Маса, кг
Ст1-А	1	□100×3, L = 4 364	1	39,08	39,1
	П1	Опорна плита бази −16×300×300	1	10,95	10,9
	Р1	Ребро бази −8×100×150	3	0,75	2,3
	Р2-А	Ребро під підкіс, ряд А −8×100×144	1	0,45	0,5
		Маса марки Ст1-А, кг (на 10 шт. — 527)			52,7
Ст1-Б	1	□100×3, L = 6 459	1	57,84	57,8
	П1	Опорна плита бази −16×300×300	1	10,95	10,9
	Р1	Ребро бази −8×100×150	3	0,75	2,3
	Р2-Б	Ребро під підкіс, ряд Б −8×100×144	1	0,45	0,5
		Маса марки Ст1-Б, кг (на 10 шт. — 715)			71,5

Зм.	Кільк.	Арк.	№ док.	Підпис	Дата
Розробив					
Перевірив					
Н. контр.					
ГІП					

36/26-КМД

Улаштування джерела резервного живлення модульної сонячної електростанції (СЕС), сел. Гостомель, вул. Свято-Покровська, 81Б

Стадія	Аркуш	Аркушів
Р	3	12

Стійки Ст1-А, Ст1-Б

Формат А3