

Балки Б1 (□120×5) — розмітка осей крокв Б2 і стійок; стики над стійками осей 3, 5, 7, 9


Б1-1 — балка поздовжня, крайня (вісь 1), 2 шт. □120×5, L = 11 560

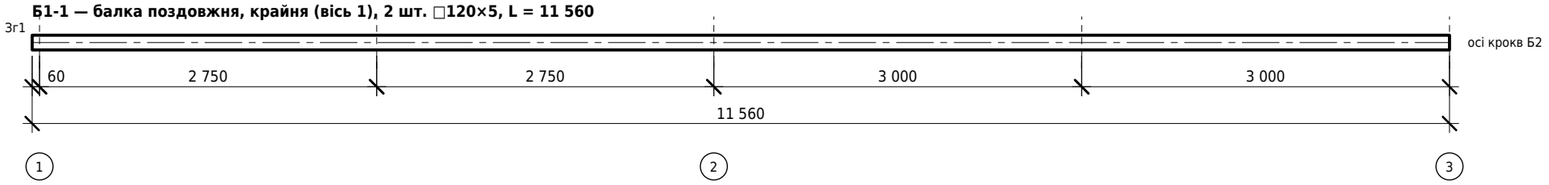

Б1-2 — балка поздовжня, середня, 6 шт. □120×5, L = 12 000

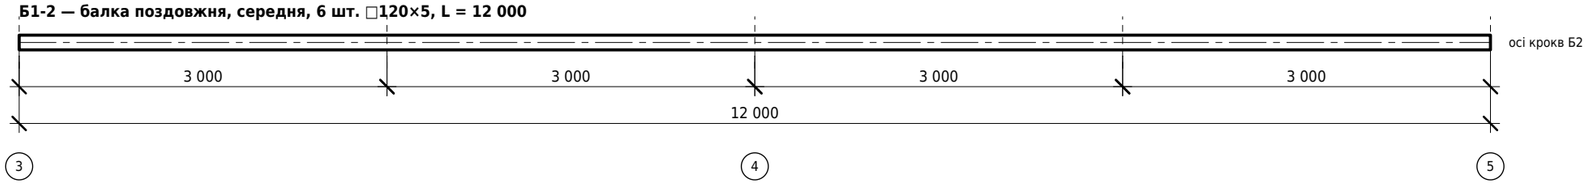


Б1-3 — балка поздовжня, крайня (вісь 10), 2 шт. □120×5, L = 5 560

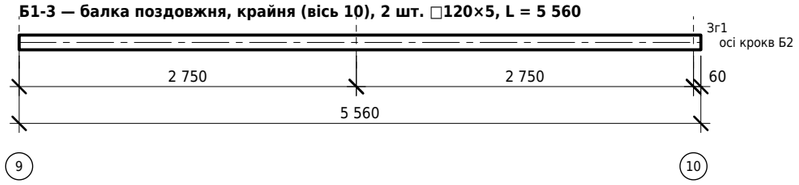


Марка	Поз.	Найменування	К-сть	Маса 1 шт., кг	Маса, кг
Б1-1	1	□120×5, L = 11 560	1	202,87	202,9
	Зг1	Заглушка □120×120 −3×120×120	1	0,34	0,3
		Маса марки Б1-1, кг (на 2 шт. — 406)			203,2
Б1-2	1	□120×5, L = 12 000	1	210,60	210,6
		Маса марки Б1-2, кг (на 6 шт. — 1 264)			210,6
Б1-3	1	□120×5, L = 5 560	1	97,58	97,6
	Зг1	Заглушка □120×120 −3×120×120	1	0,34	0,3
		Маса марки Б1-3, кг (на 2 шт. — 196)			97,9

Прогони Пр1 (□120×60×4, висотою 120 перпендикулярно до скату) — розмітка осей крокв; стики над кроквами осей 3, 5, 7, 9


Пр1-1 — прогін, крайній (вісь 1), 8 шт. □120×60×4, L = 11 560

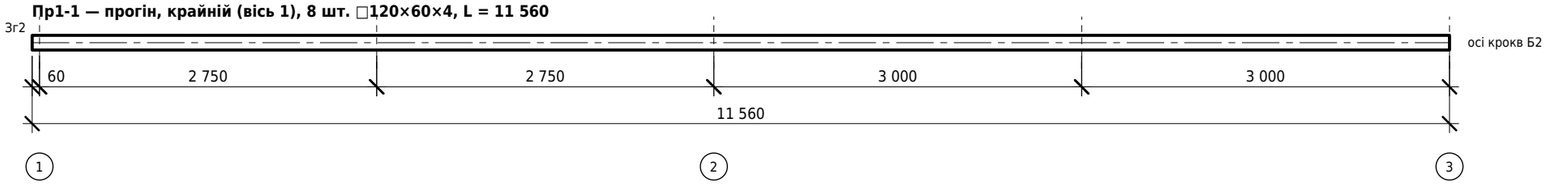

Пр1-2 — прогін, середній, 24 шт. □120×60×4, L = 12 000

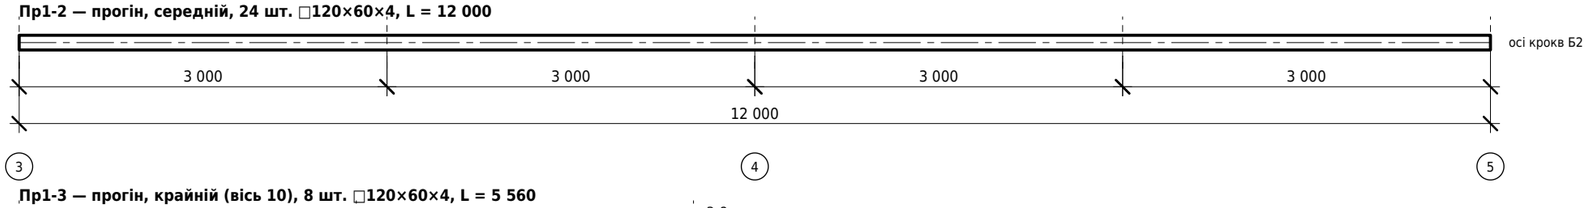

Пр1-3 — прогін, крайній (вісь 10), 8 шт. □120×60×4, L = 5 560

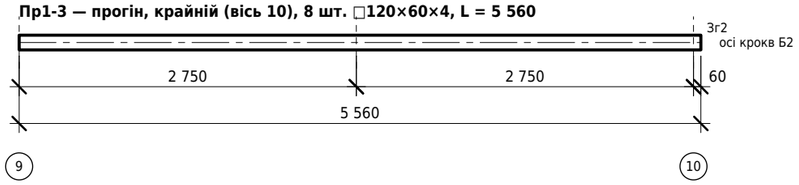

Марка	Поз.	Найменування	К-сть	Маса 1 шт., кг	Маса, кг
Пр1-1	1	□120×60×4, L = 11 560	1	121,13	121,1
	Зг2	Заглушка □120×60 −3×120×60	1	0,17	0,2
		Маса марки Пр1-1, кг (на 8 шт. — 970)			121,3
Пр1-2	1	□120×60×4, L = 12 000	1	125,74	125,7
		Маса марки Пр1-2, кг (на 24 шт. — 3 018)			125,7
Пр1-3	1	□120×60×4, L = 5 560	1	58,26	58,3
	Зг2	Заглушка □120×60 −3×120×60	1	0,17	0,2
		Маса марки Пр1-3, кг (на 8 шт. — 467)			58,4

1. Б1-1 і Пр1-1 — від осі 1 з виступом 60 мм (врівень із зовнішньою гранню крайньої крокви), Б1-3 і Пр1-3 — так само за віссю 10.
2. Б1-2 і Пр1-2 — цілий хлист 12 000. Стики — з повним проваром; на верхній грані Б1 у місці спирання крокви шов зачистити врівень.
3. Відкриті торці (позначено «Зг1», «Зг2») закрити заглушками Зг1 (Б1) і Зг2 (Пр1), арк. 8.
4. Пр1 приварюються до крокв на монтажі, кріплення притисків модулів — див. загальні вказівки, п. 10.

Зм.	Кільк.	Арк.	№ док.	Підпис	Дата
Розробив					
Перевірив					
Н. контр.					
ГІП					

36/26-КМД

Улаштування джерела резервного живлення модульної сонячної електростанції (СЕС), сел. Гостомель, вул. Свято-Покровська, 81Б

Стадія	Аркуш	Аркушів
Р	4	12

Балки Б1, прогони Пр1

Формат А3