


Кроква Б2 (19 шт.) — положення як у розрізі 1-1 М 1:25

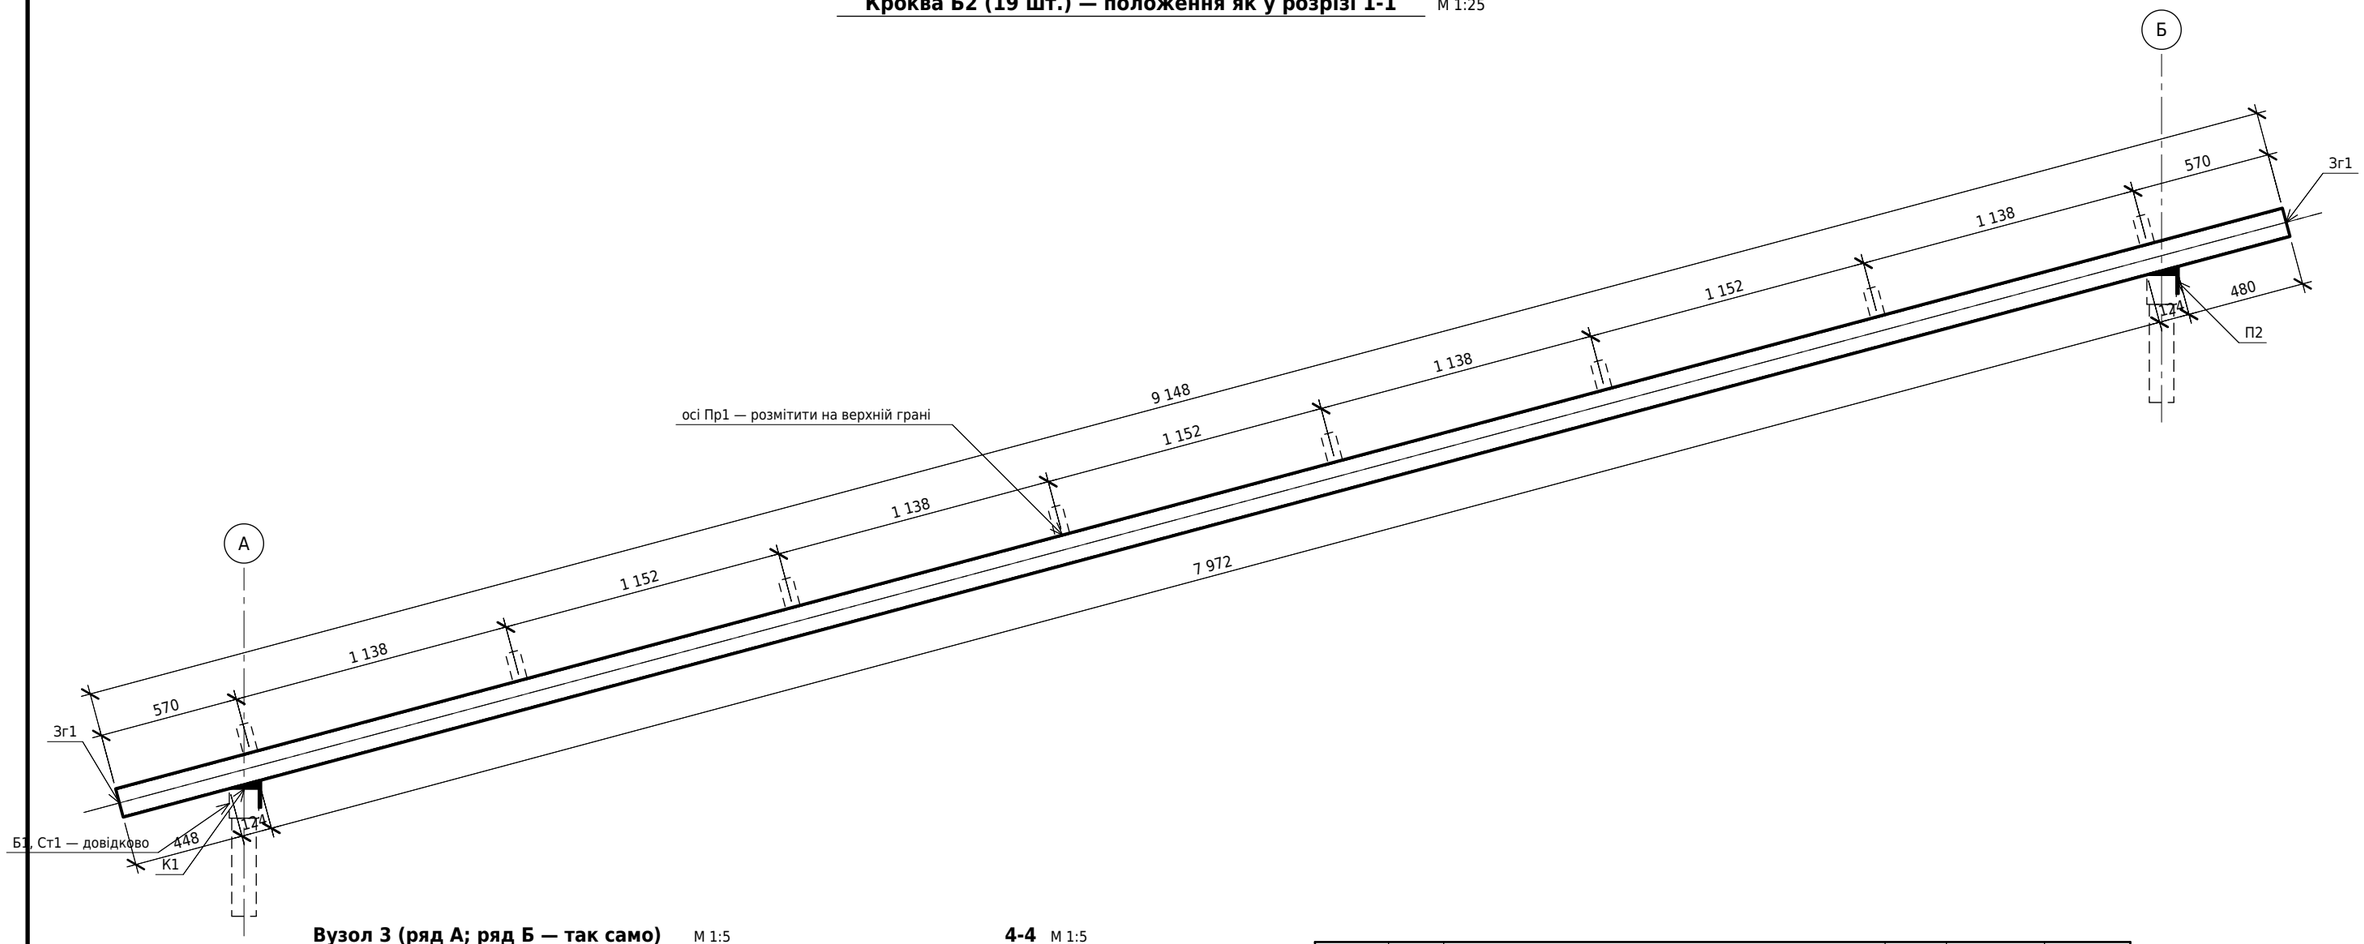

Вузол 3 (ряд А; ряд Б — так само) М 1:5

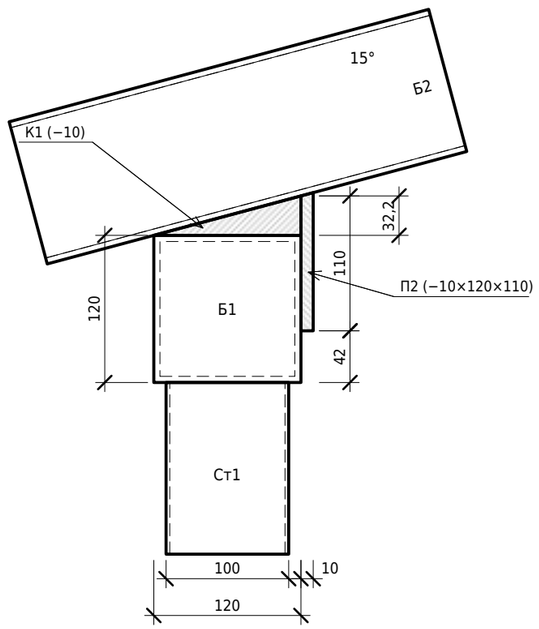

4-4 М 1:5

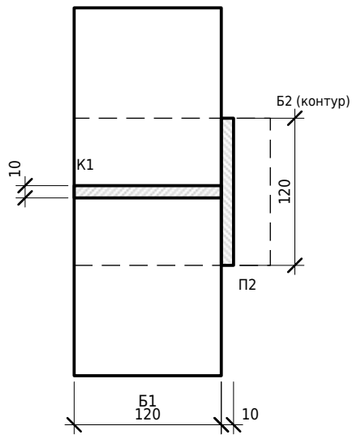

Марка	Поз.	Найменування	К-сть	Маса 1 шт., кг	Маса, кг
Б2	1	□120×5, L = 9 148	1	160,54	160,5
	К1	Клин під кроку −10×120×32,2	2	0,15	0,3
	П2	Бічна пластина вузла кроки −10×120×110	2	1,04	2,1
	Зг1	Заглушка □120×120 −3×120×120	2	0,34	0,7
		Маса марки Б2, кг (на 19 шт. — 3 108)			163,6

1. Кроква спирається на Б1 нижнім ребром; клин К1 заповнює зазор до 32,2 мм над Б1.
2. К1 і П2 приварити до кроки в заводі (kf = 4, з двох боків); до Б1 — на монтажі (kf = 4).
3. Торці кроки — під 90° до осі, заглушки Зг1. Прогони Пр1 приварюються на монтажі.

Зм.	Кільк.	Арк.	№ док.	Підпис	Дата
Розробив					
Перевірив					
Н. контр.					
ГІП					

36/26-КМД

Улаштування джерела резервного живлення модульної сонячної електростанції (СЕС), сел. Гостомель, вул. Свято-Покровська, 81Б

Стадія	Аркуш	Аркушів
Р	5	12

Кроква Б2. Вузол 3

Формат А3