
Вв1-А — Підкіс рами від ряду А, 10 шт., □100×3, заготовка L = 6 755



низ (вузол 1): торець вертикальний, по грані стійки

верх (вузол 2): торець по низу крокви Б2


Вв1-Б — Підкіс рами від ряду Б, 10 шт., □100×3, заготовка L = 6 757

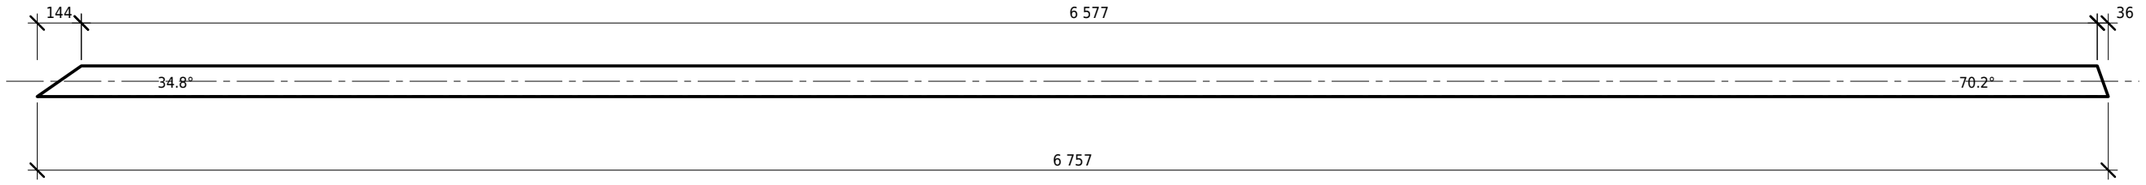


низ (вузол 1): торець вертикальний, по грані стійки

верх (вузол 2): торець по низу крокви Б2

Вузол 1 (ряд А) М 1:5

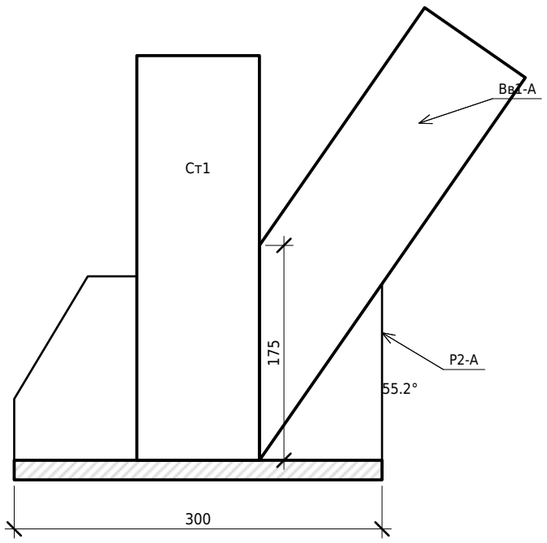

Вузол 2 М 1:5

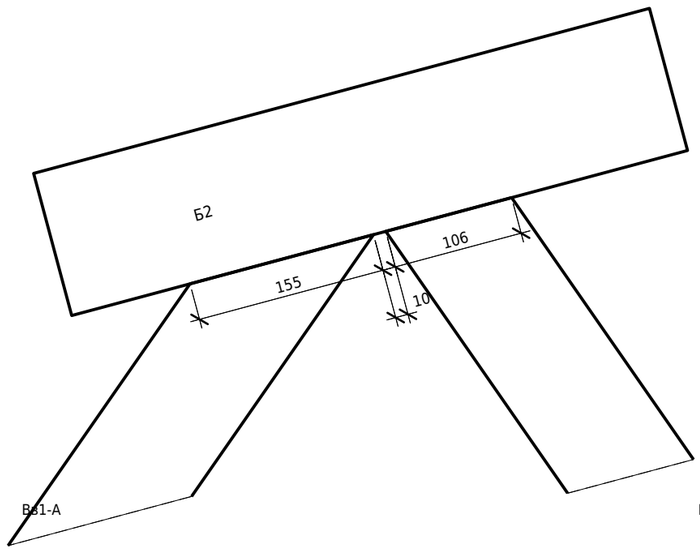

Марка	Поз.	Найменування	К-сть	Маса 1 шт., кг	Маса, кг
Вв1-А	1	□100×3, L = 6 755	1	59,32	59,3
		Маса марки Вв1-А, кг (на 10 шт. — 593)			59,3
Вв1-Б	1	□100×3, L = 6 757	1	59,70	59,7
		Маса марки Вв1-Б, кг (на 10 шт. — 597)			59,7

Монтажні шви: Вв1 до Ст1, Р2 і П1 — kf = 4.

Вершина — посередині прольоту (3 910 від осі А).

Монтажні шви підкосів до крокви — kf = 4 по контуру.

Зм.	Кільк.	Арк.	№ док.	Підпис	Дата
Розробив					
Перевірив					
Н. контр.					
ГІП					

36/26-КМД

Улаштування джерела резервного живлення модульної сонячної електростанції (СЕС), сел. Гостомель, вул. Свято-Покровська, 81Б

Стадія	Аркуш	Аркушів
Р	6	12

Підкоси Вв1-А, Вв1-Б. Вузли 1, 2