Ферма ряду Б — проліт 6,0 м (проліт 5,5 м — аналогічно) М 1:25

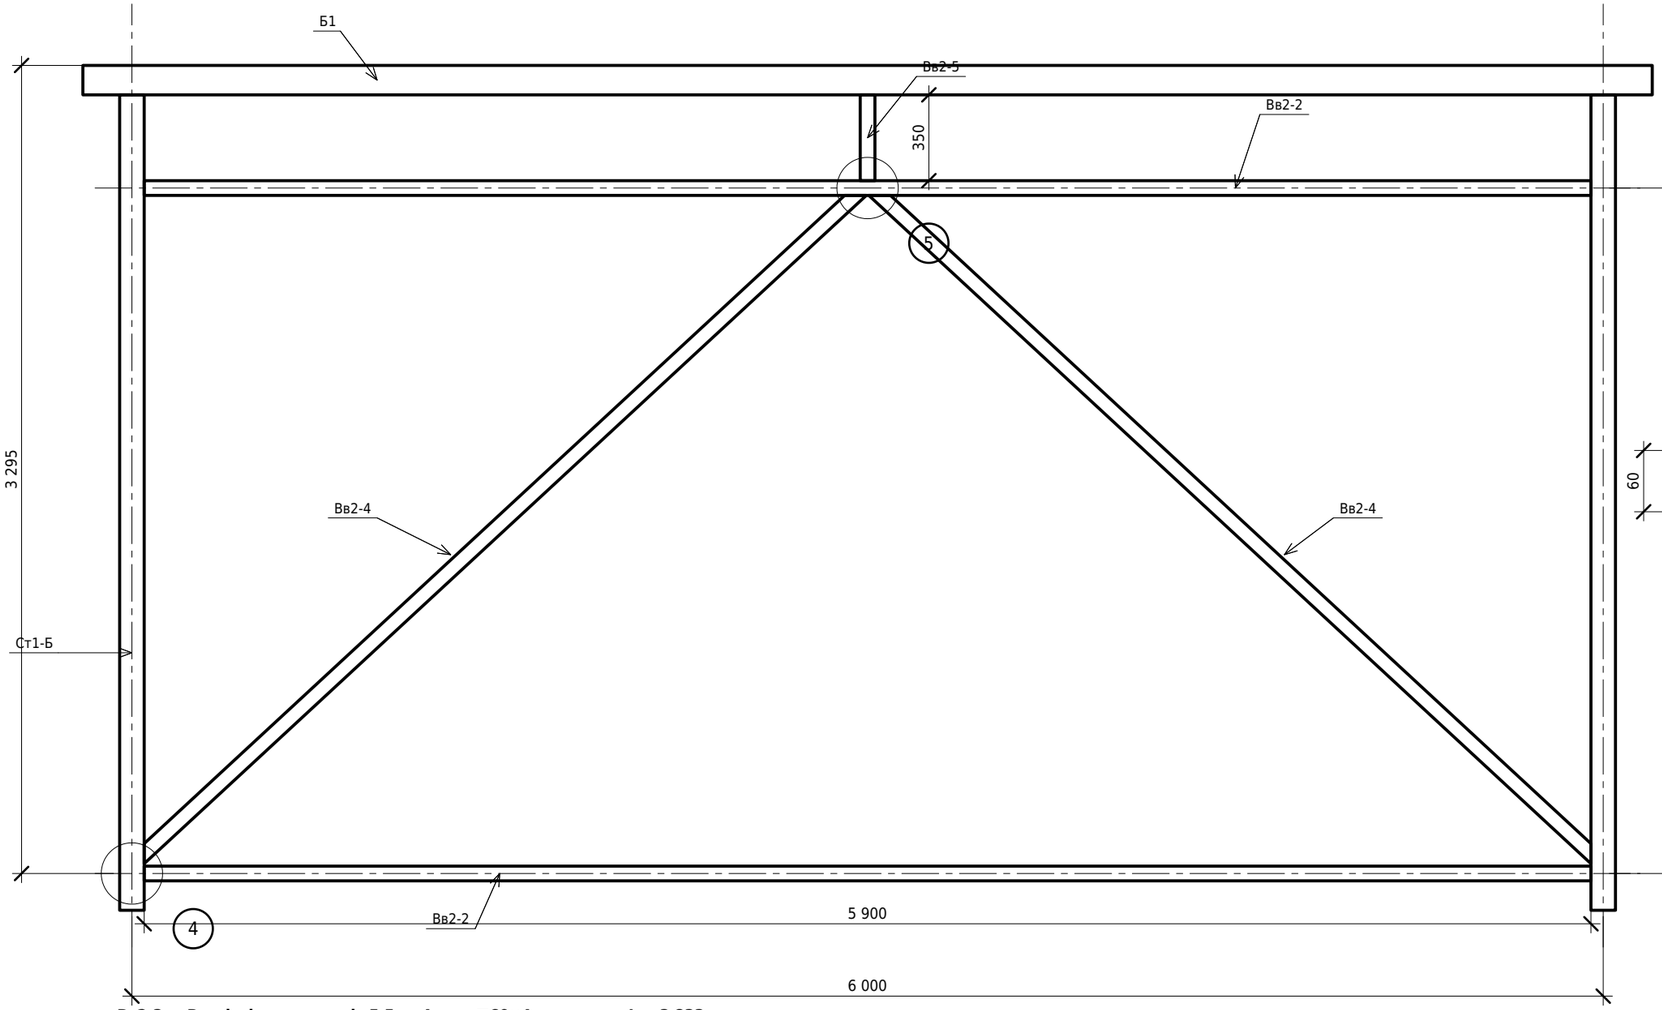

Вузол 4 М 1:6

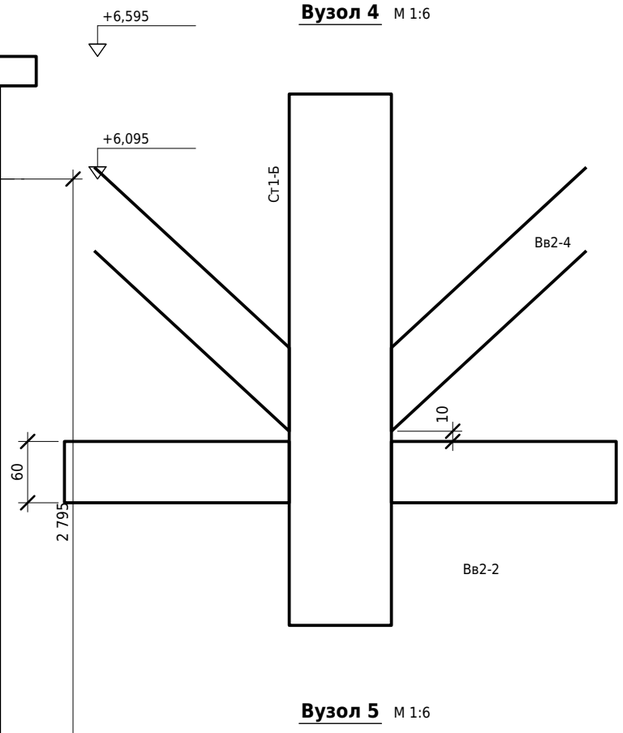

Вузол 5 М 1:6

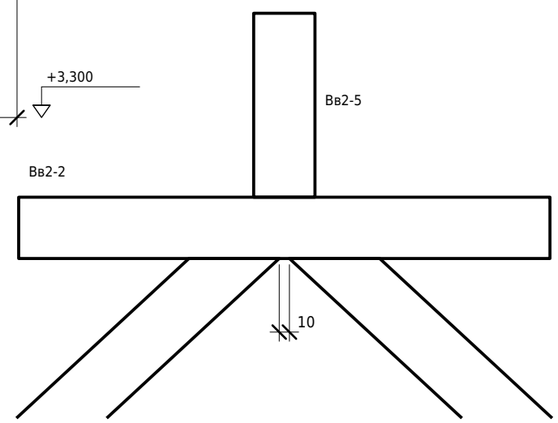

Вв2-3 — Розкіс ферми, проліт 5,5 м, 4 шт., □60×4, заготовка L = 3 833

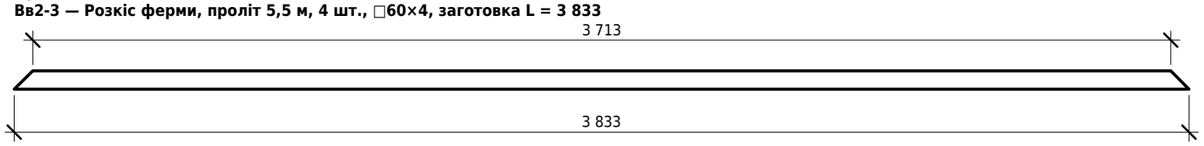

низ: торець вертикальний (44.7° до грані); верх: торець горизонтальний (45.3°)

Вв2-4 — Розкіс ферми, проліт 6,0 м, 14 шт., □60×4, заготовка L = 4 012

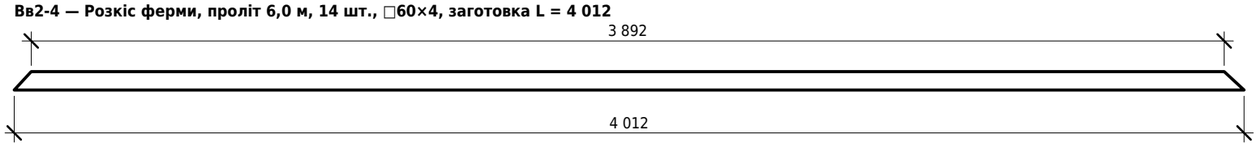

низ: торець вертикальний (47.2° до грані); верх: торець горизонтальний (42.8°)

Шви ферми — на монтажі, kf = 4 по контуру.

Пояси — від грані до грані стійок.

Зм.	Кільк.	Арк.	№ док.	Підпис	Дата
Розробив					
Перевірив					
Н. контр.					
ГІП					

36/26-КМД

Улаштування джерела резервного живлення модульної сонячної електростанції (СЕС), сел. Гостомель, вул. Свято-Покровська, 81Б

Стадія	Аркуш	Аркушів
Р	7	12

Ферма Вв2 ряду Б. Вузли 4, 5

Формат А3